

UNIT 11, MORTIMER'S TRADING ESTATE, ROMSEY ROAD, OWES, HAMPSHIRE, SO5 0AL


TEL: 0282 000077
EMAIL: ENQURIES@REGENCYFACADES.CO.UK
WEB: WWW.REGENCYFACADES.CO.UK

COPYRIGHT NOTE:
THIS DRAWING AND ITS CONTENT IS COPYRIGHT OF REGENCY FACADES LIMITED.
ALL RIGHTS RESERVED.
ANY REDISTRIBUTION OR REPRODUCTION OF PART OR ALL OF THE CONTENTS IN ANY FORM IS PROHIBITED AND YOU MAY NOT EXCEPT WITH WRITTEN PERMISSION FROM REGENCY FACADES LIMITED.

Notes:


HATCH DENOTES EXISTINGWORKS BY OTHERS

RFL DRAWINGS ARE SHOWING INDICATIVE INTERNAL FINISHES.
INTERNAL FIT OUT COMPANY TO PROVIDE PROJECT RELATED DRAWINGS FOR REVIEW.
ANY COMMENTS RELATING TO INTERNAL FINISHES WILL BE IGNORED.

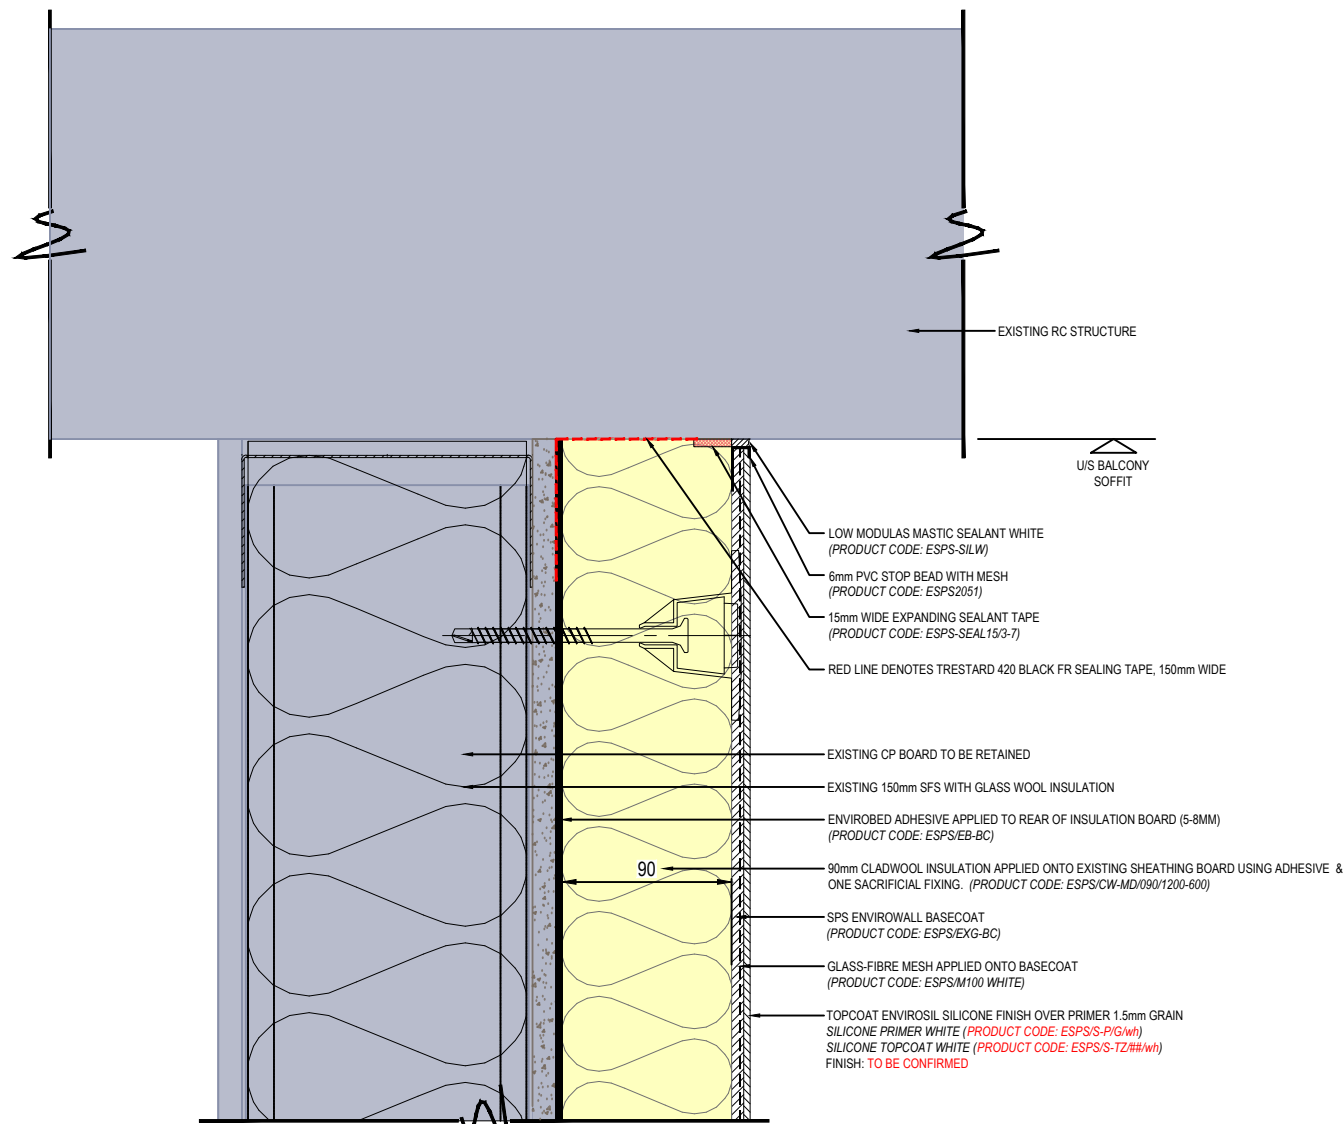


01 CROSS SECTION - RENDER / EXISTING BALCONY STRUCTURE DETAIL

Scale 1:2

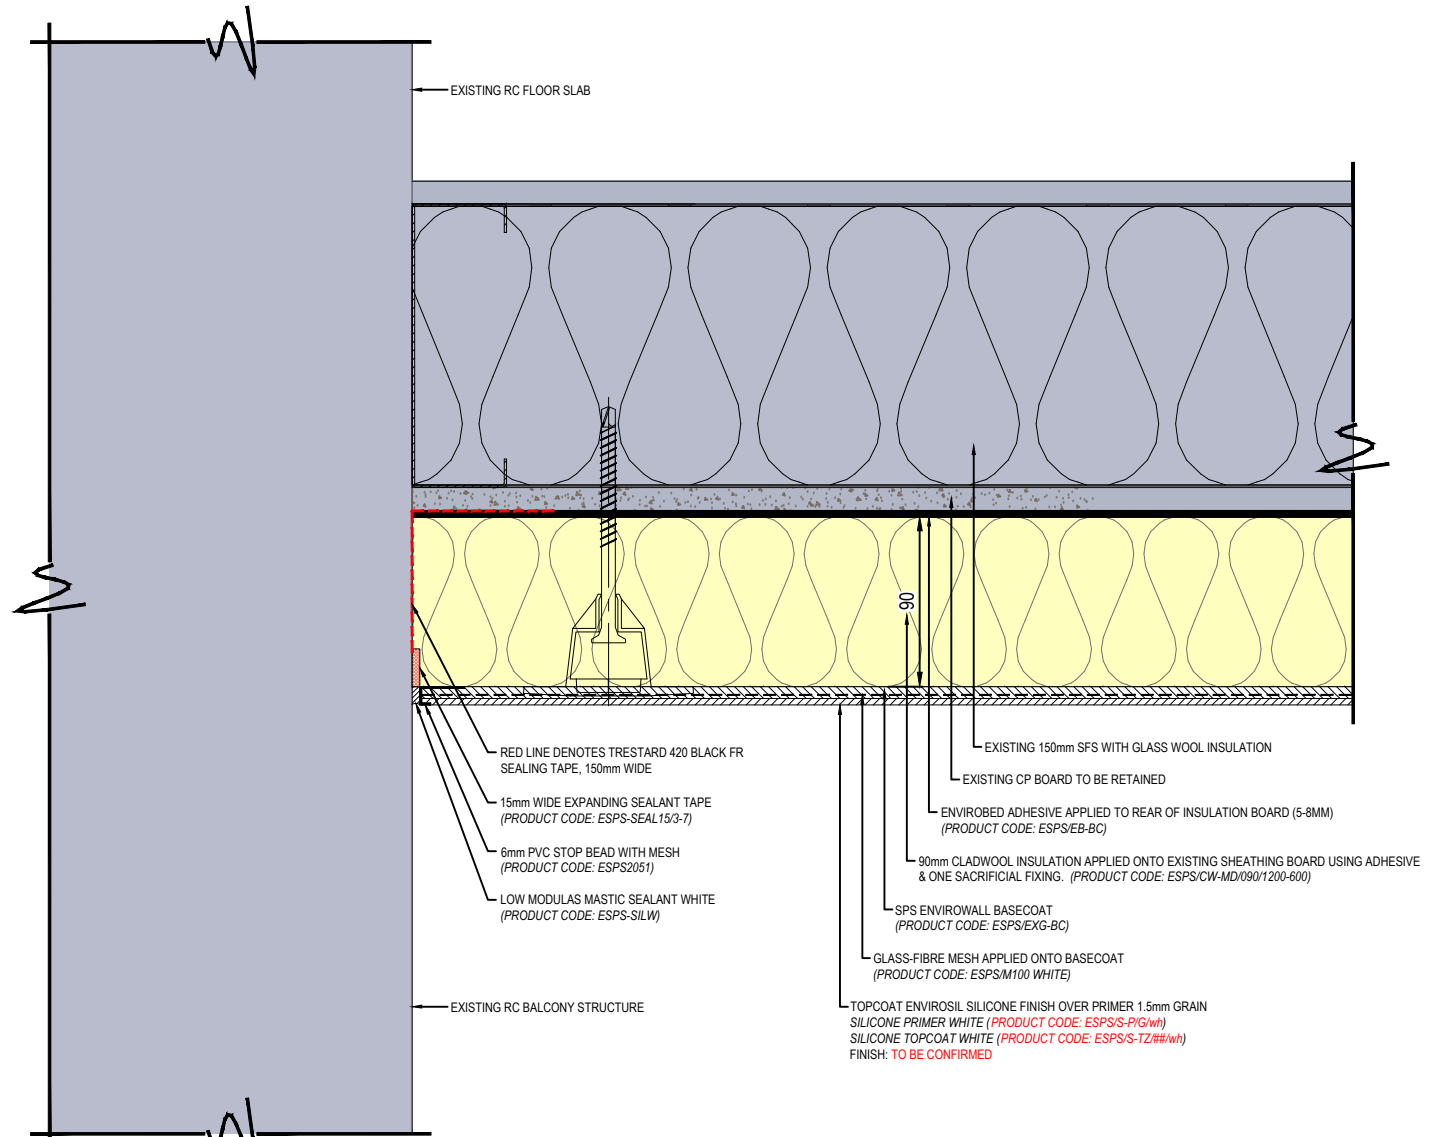

02 PLAN SECTION - RENDER / EXISTING BALCONY STRUCTURE DETAIL

Scale 1:2

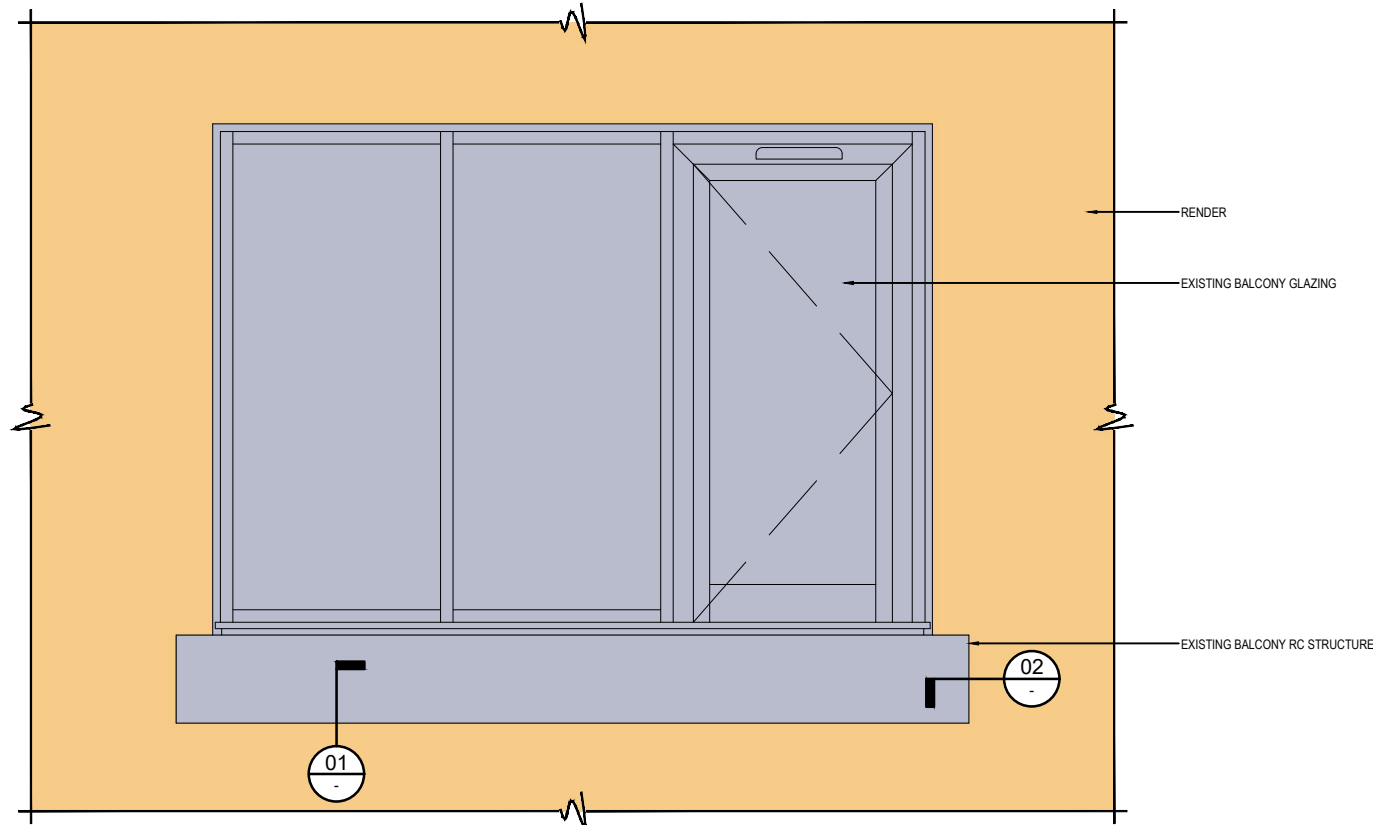

03 PART ELEVATION - RENDER / EXISTING BALCONY

Scale 1:15



FITTERS NOTE

THIS DRAWING IS TO BE READ IN CONJUNCTION WITH RENDER SPECIFICATION DRAWING No. TSB-RFL-ZZ-ZZ-DR-W-001201

REV	DATE	DESCRIPTION	BY	CHECKED	DATE
01	10/07/2025	ISSUED FOR CONSTRUCTION	BB	MHY	
02	10/07/2025	REVISION	BB	MHY	

FOR CONSTRUCTION

Client: BARRATT REDROW

Project: 1761 THE SUMMIT

Title: RENDER SYSTEM BALCONY RENDER INTERFACE DETAILS

Drawn By: BB

Checked By: MHY

Scale: 1:2 @ A1

Date: 10/07/2025

TSB-RFL-ZZ-ZZ-DR-W-003005 C01