



Key Plan:

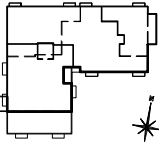

UNIT 11, MORTIMER'S TRADING ESTATE, ROMSEY ROAD,
LOWES, HAMPSHIRE, SO51 6AL.
TEL: 02882 000077
EMAIL: ENQURIES@REGENCYFACADES.CO.UK
WWW.REGENCYFACADES.CO.UK

COPYRIGHT NOTE:
THIS DRAWING AND ITS CONTENT IS COPYRIGHT OF
REGENCY FACADES LIMITED.
ALL RIGHTS RESERVED.
ANY REDISTRIBUTION OR REPRODUCTION OF PART OR ALL
OF THE CONTENTS IN ANY FORM IS PROHIBITED AND YOU
MAY NOT EXCEPT WITH WRITTEN PERMISSION FROM
REGENCY FACADES LIMITED.

Notes:
HATCH DENOTES EXISTINGWORKS
BY OTHERS
RFL DRAWINGS ARE SHOWING INDICATIVE
INTERNAL FINISHES.
INTERNAL FIT OUT COMPANY TO PROVIDE
PROJECT RELATED DRAWINGS FOR REVIEW.
ANY COMMENTS RELATING TO INTERNAL
FINISHES WILL BE IGNORED.

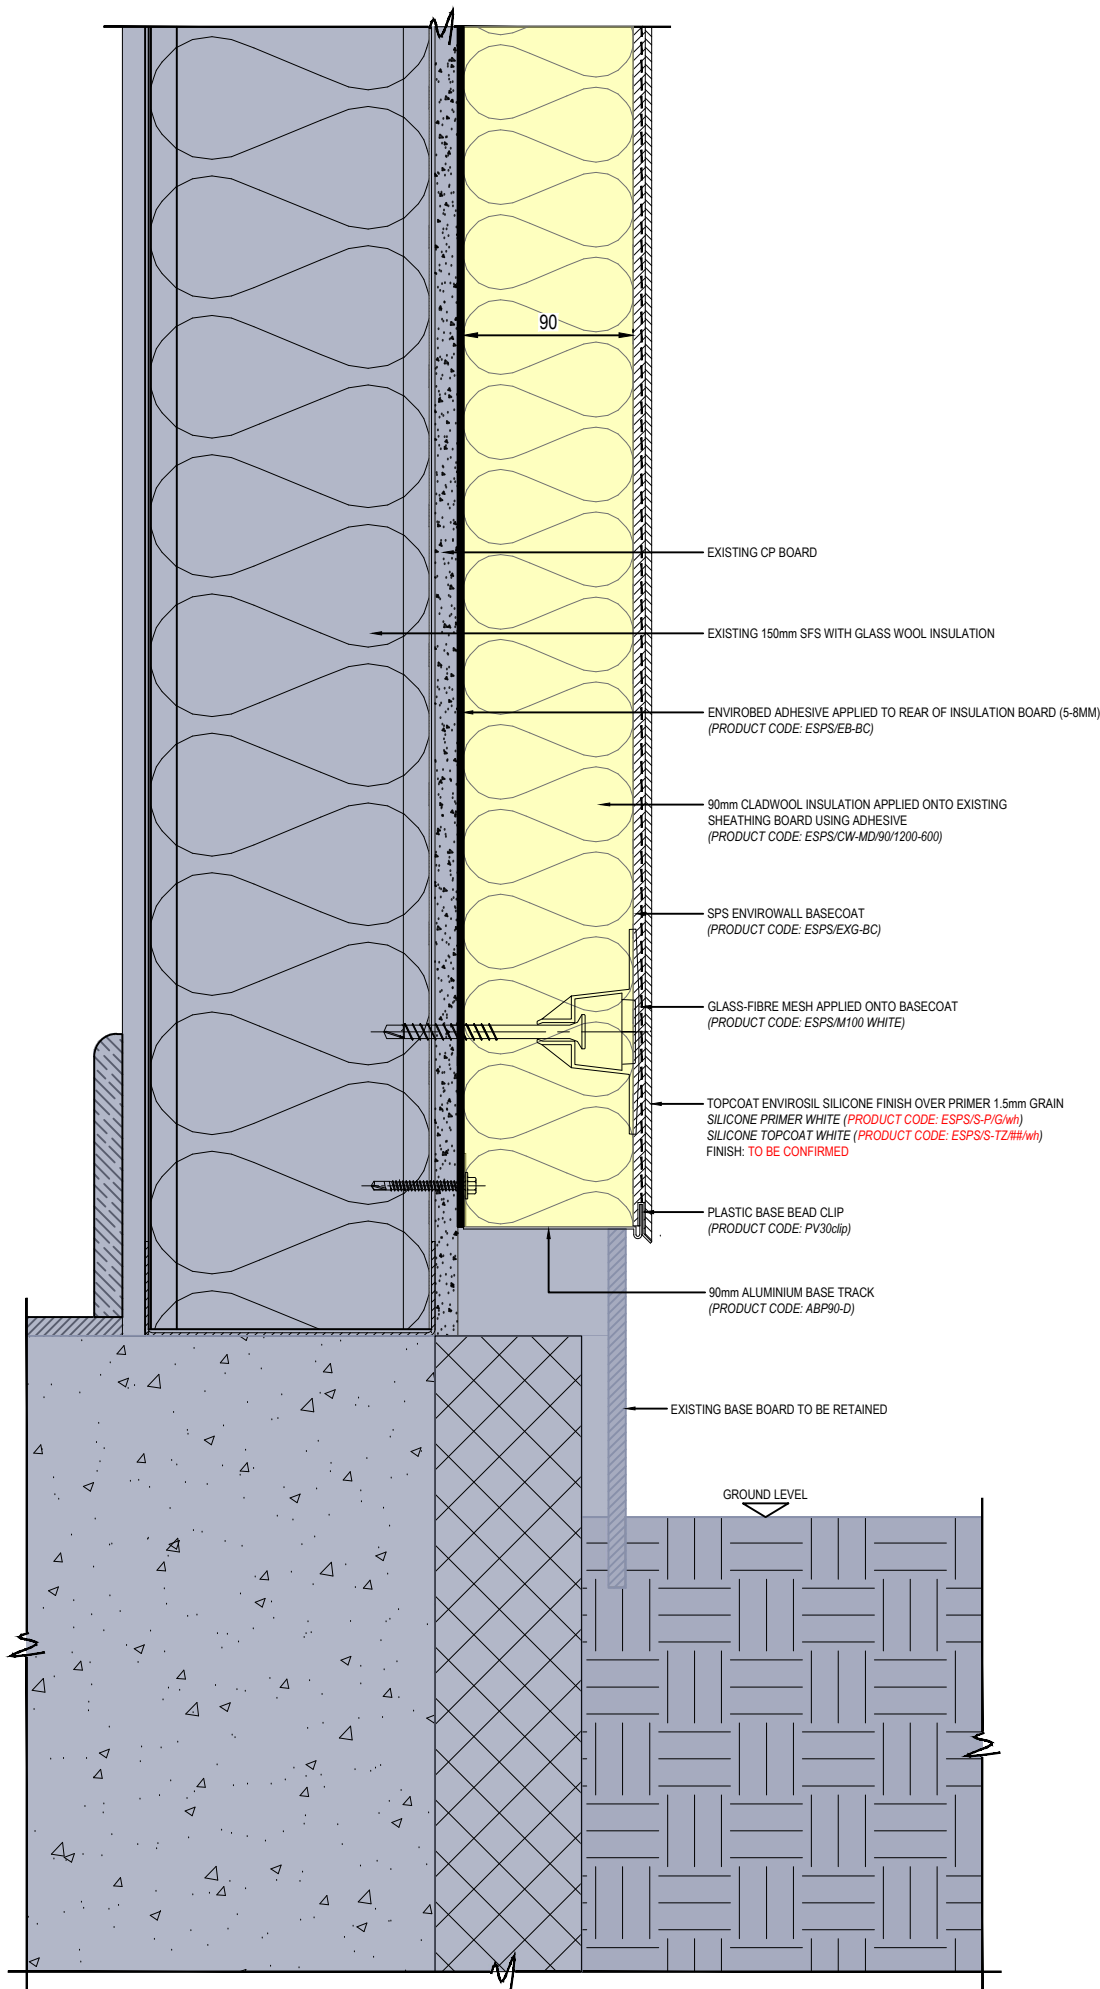

01 PLAN SECTION - RENDER / BOARD TO RAISED BEDS
Scale 1:2



FITTERS NOTE
THIS DRAWING IS TO BE READ IN CONJUNCTION WITH RENDER
SPECIFICATION DRAWING No. TSB-RFL-ZZ-ZZ-DR-W-001201

REV	DATE	DESCRIPTION	BY	CHECKED BY
001	05/08/2025	ISSUED FOR CONSTRUCTION	BB	MHY
002	05/08/2025	REVISION	BB	MHY

FOR CONSTRUCTION

Client	BARRATT REDROW
Project	1761 THE SUMMIT
Title	RENDER SYSTEM GROUND LEVEL BASE DETAILS BOARD TO RAISED BEDS
Drawn By	BB
Checked By	MHY
Scale	1:2 @ A1
Date	05/08/2025
TSB-RFL-ZZ-ZZ-DR-W-003006	C01