



Key Plan:

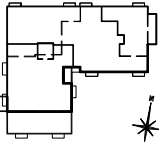

UNIT 11, MORTIMER'S TRADING ESTATE, ROMSEY ROAD,
LOWES, HAMPSHIRE, SO51 5AL
TEL: 02382 000077
EMAIL: ENQU@REGENCYFACADES.CO.UK
WWW.REGENCYFACADES.CO.UK

COPYRIGHT NOTE:
THIS DRAWING AND ITS CONTENT IS COPYRIGHT OF
REGENCY FACADES LIMITED.
ALL RIGHTS RESERVED.
ANY REPRODUCTION OR REPRODUCTION OF PART OR ALL
OF THE CONTENTS IN ANY FORM IS PROHIBITED AND YOU
MAY NOT EXCEPT WITH WRITTEN PERMISSION FROM
REGENCY FACADES LIMITED.

Notes:
HATCH DENOTES EXISTING WORKS
BY OTHERS
RFL DRAWINGS ARE SHOWING INDICATIVE
INTERNAL FINISHES.
INTERNAL FIT OUT COMPANY TO PROVIDE
PROJECT RELATED DRAWINGS FOR REVIEW.
ANY COMMENTS RELATING TO INTERNAL
FINISHES WILL BE IGNORED.

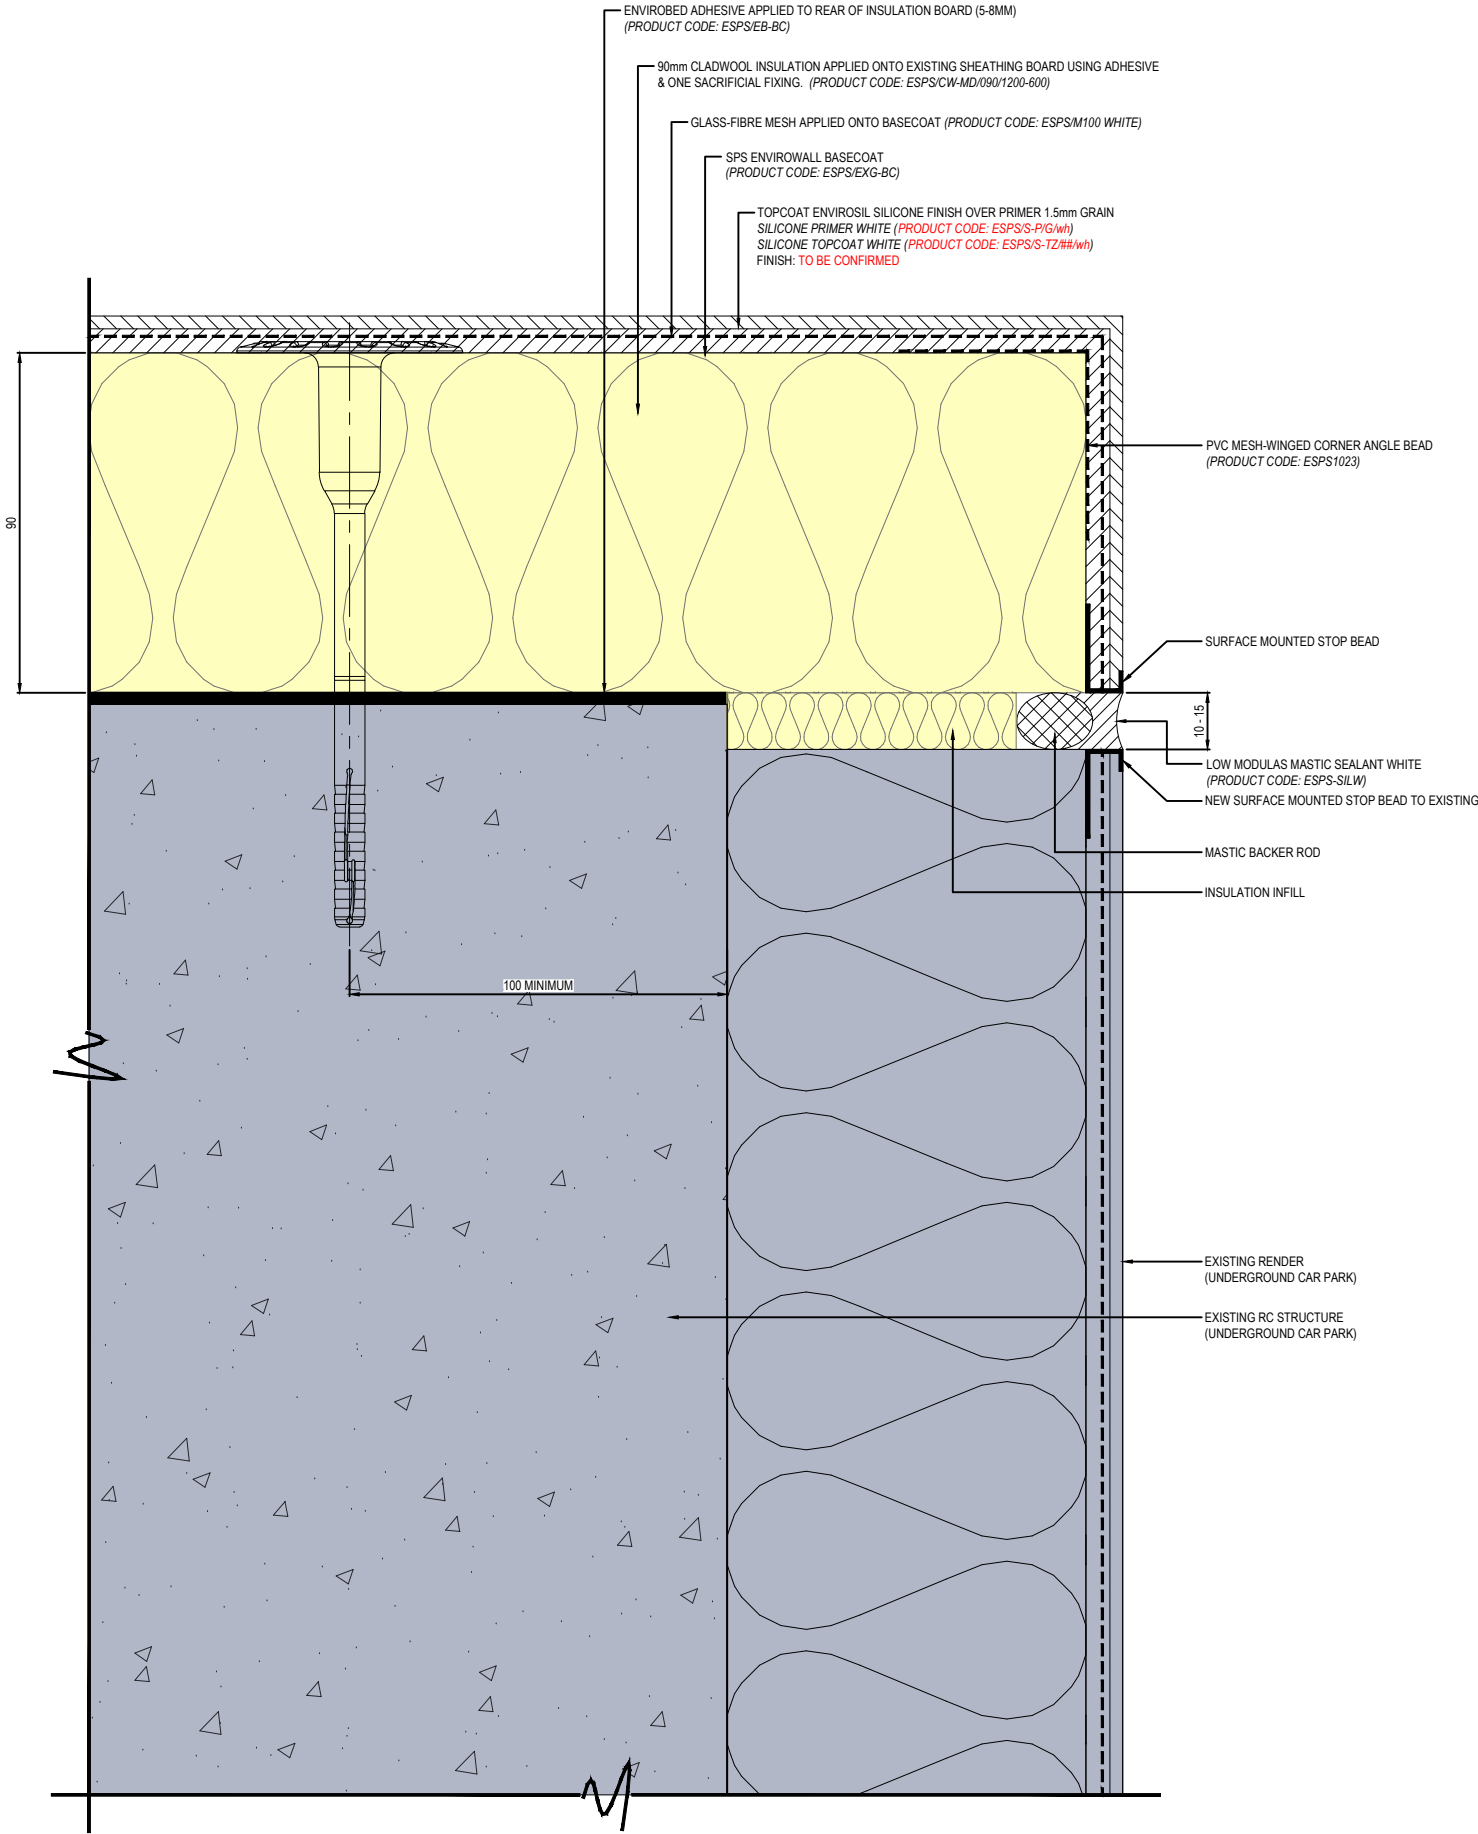

01 PLAN SECTION - RENDER - NEW TO EXISTING DETAIL
Scale 1:1



FITTERS NOTE
THIS DRAWING IS TO BE READ IN CONJUNCTION WITH RENDER
SPECIFICATION DRAWING No. TSB-RFL-ZZ-ZZ-DR-W-001201 &

REV	DATE	DESCRIPTION	BY	CHKD
01	28/07/2025	ISSUED FOR CONSTRUCTION	BB	MHY
02	28/07/2025	REVISION	BB	MHY
03	28/07/2025	REVISION	BB	MHY

Client: BARRATT REDROW
Project: 1761 THE SUMMIT
Title: RENDER SYSTEM
NEW TO EXISTING JOINT DETAIL
Drawn By: BB
Checked By: MHY
Scale: 1:1 @ A1
Date: 28/07/2025
TSB-RFL-ZZ-ZZ-DR-W-003007 C01