



UNIT 11, MORTIMER'S TRADING ESTATE, ROMSEY ROAD,
LOWES, HAMPSHIRE, SO51 5AL.
TEL: 0282 000077
EMAIL: ENQUIRE@REGENCYFACADES.CO.UK
WWW.REGENCYFACADES.CO.UK

COPYRIGHT NOTE:
THIS DRAWING AND ITS CONTENT IS COPYRIGHT OF
REGENCY FACADES LIMITED.
ALL RIGHTS RESERVED.
ANY REDISTRIBUTION OR REPRODUCTION OF PART OR ALL
OF THE CONTENTS IN ANY FORM IS PROHIBITED AND YOU
MAY NOT EXCEPT WITH WRITTEN PERMISSION FROM
REGENCY FACADES LIMITED.


Notes:
■ HATCH DENOTES EXISTINGWORKS
BY OTHERS
RFL DRAWINGS ARE SHOWING INDICATIVE
INTERNAL FINISHES.
INTERNAL FIT OUT COMPANY TO PROVIDE
PROJECT RELATED DRAWINGS FOR REVIEW.
ANY COMMENTS RELATING TO INTERNAL
FINISHES WILL BE IGNORED.

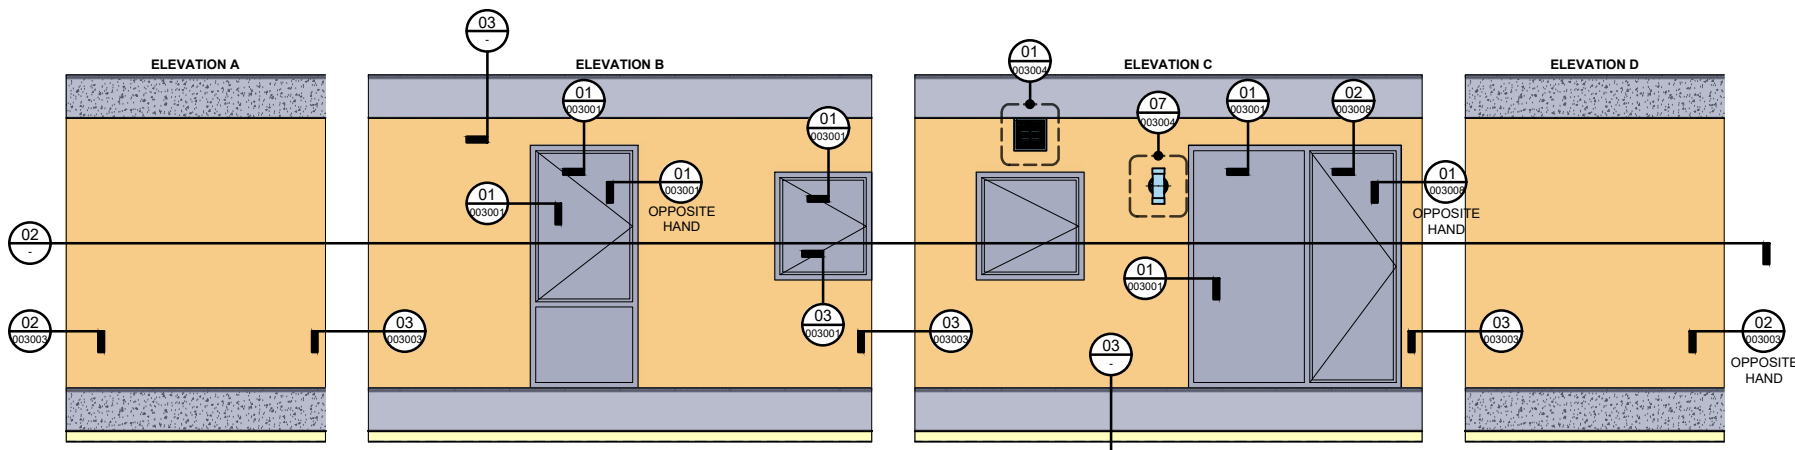

01 UNROLLED ELEVATIONS - RENDER / RECESSED BALCONY
Scale 1:35

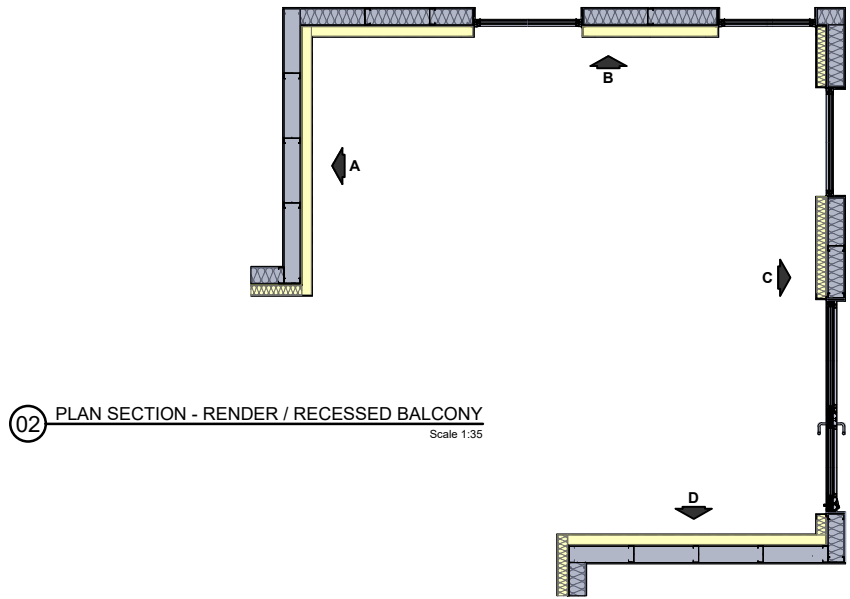

02 PLAN SECTION - RENDER / RECESSED BALCONY
Scale 1:35

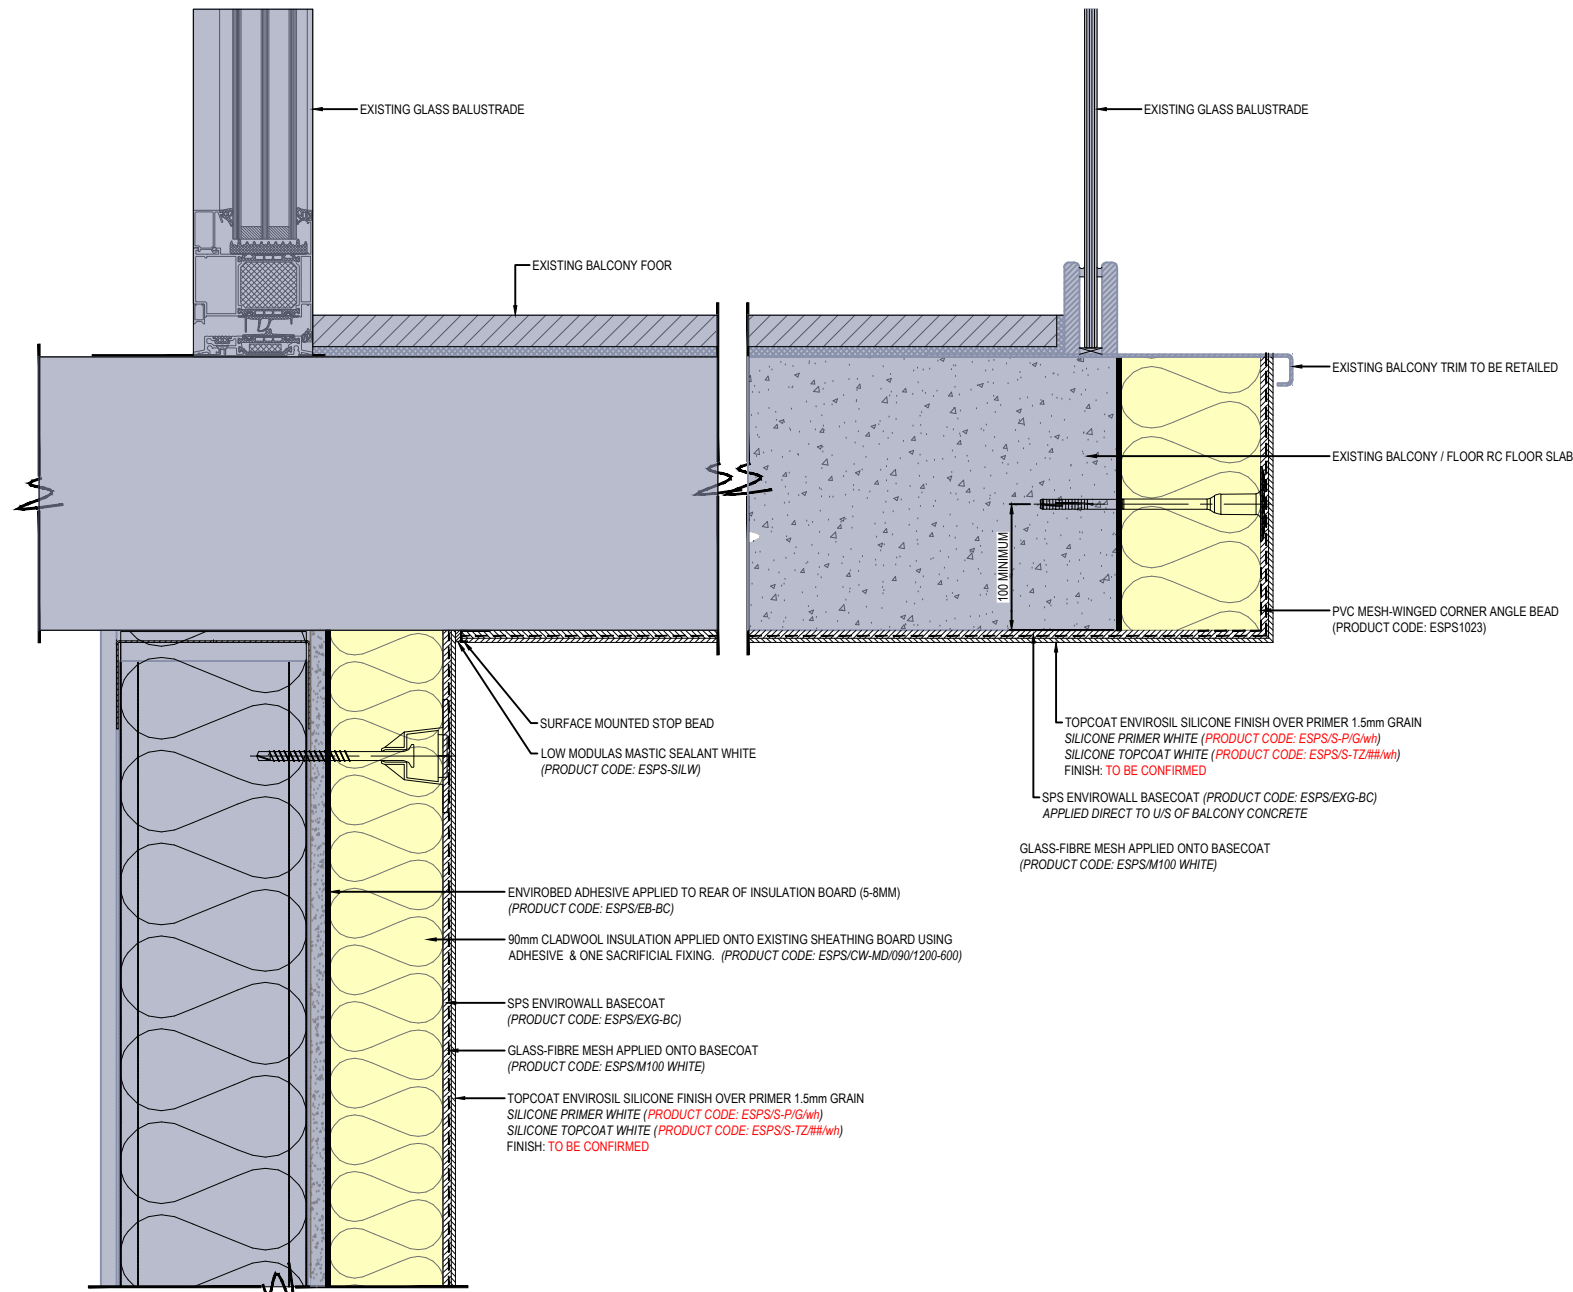

03 CROSS SECTION - RENDER / RECESSED BALCONY
Scale 1:3



FITTERS NOTE
THIS DRAWING IS TO BE READ IN CONJUNCTION WITH RENDER
SPECIFICATION DRAWING No. TSB-RFL-ZZ-ZZ-DR-W-001201

REV	DATE	DESCRIPTION	BY	CHECKED	DATE
001	12/08/2025	ISSUED FOR CONSTRUCTION	BB	MHY	
002	12/08/2025	ISSUED FOR CONSTRUCTION	BB	MHY	
003	12/08/2025	ISSUED FOR CONSTRUCTION	BB	MHY	

FOR CONSTRUCTION

Client: BARRATT REDROW
Project: 1761 THE SUMMIT
Title: RENDER SYSTEM
RECESSED BALCONY DETAILS

Drawn By: BB
Scale: 1:3 & 1:35 @ A1
Checked By: MHY
Date: 12/08/2025
TSB-RFL-ZZ-ZZ-DR-W-003009 C01
ISSUED FOR CONSTRUCTION