


UNIT 11, MORTIMER TRADING ESTATE, ROMSEY ROAD,
LOWES, HAMPSHIRE, SO51 5AL.
TEL: 02382 000077
EMAIL: ENQUIRIES@REGENCYFACADES.CO.UK
WWW.REGENCYFACADES.CO.UK

COPYRIGHT NOTE:
THIS DRAWING AND ITS CONTENT IS COPYRIGHT OF
REGENCY FACADES LIMITED.
ALL RIGHTS RESERVED.
ANY REPRODUCTION OR REPRODUCTION OF PART OR ALL
OF THE CONTENTS IN ANY FORM IS PROHIBITED AND YOU
MAY NOT EXCEPT WITH WRITTEN PERMISSION FROM
REGENCY FACADES LIMITED.

Notes
HATCH DENOTES EXISTING WORKS
BY OTHERS
RFL DRAWINGS ARE SHOWING INDICATIVE
INTERNAL FINISHES.
INTERNAL FIT OUT COMPANY TO PROVIDE
PROJECT RELATED DRAWINGS FOR REVIEW.
ANY COMMENTS RELATING TO INTERNAL
FINISHES WILL BE IGNORED.

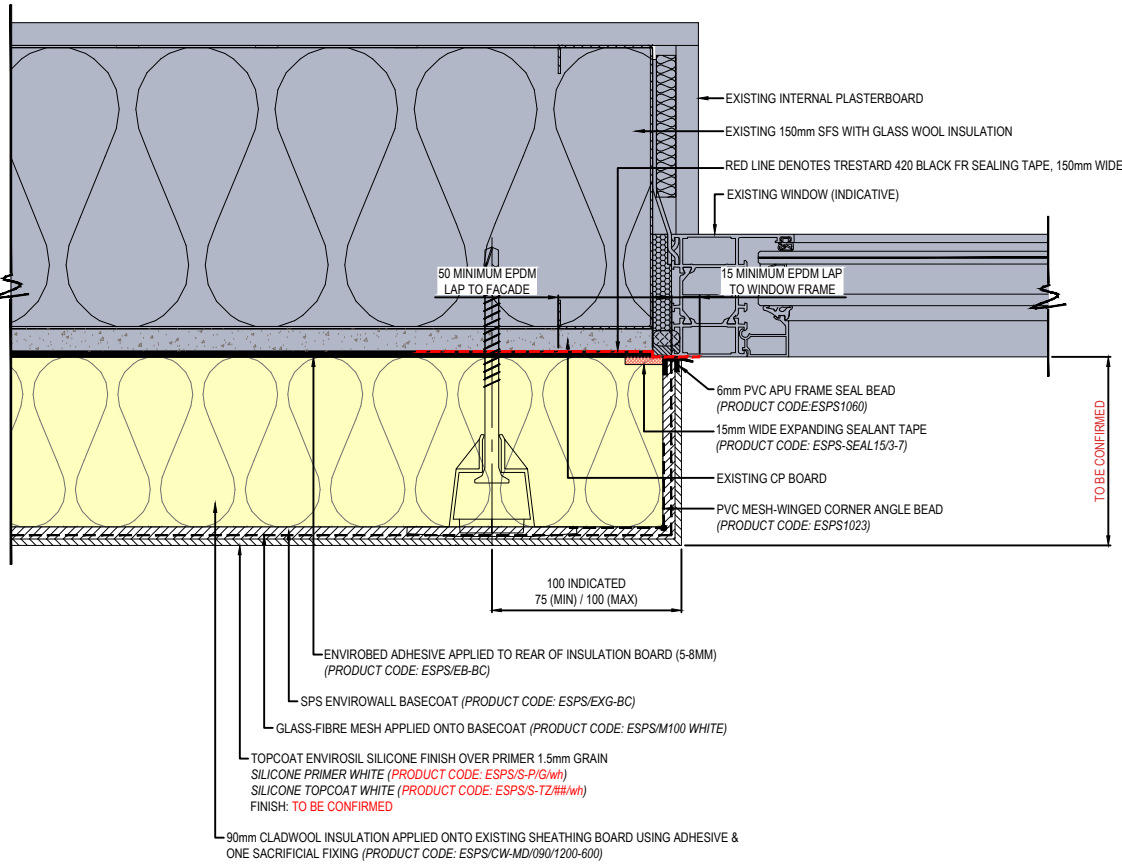

01 PLAN SECTION - RENDER / WINDOW JAMB INTERFACE DETAIL
Scale 1:2

ENVIROBED ADHESIVE APPLIED TO REAR OF INSULATION BOARD (5-8MM)
(PRODUCT CODE: ESPS/EB-BC)

90mm CLADWOOL INSULATION APPLIED ONTO EXISTING SHEATHING BOARD USING ADHESIVE
& ONE SACRIFICIAL FIXING (PRODUCT CODE: ESPS/CW-MD/090/1200-600)

SPS ENVIROWALL BASECOAT (PRODUCT CODE: ESPS/EXG-BC)

GLASS-FIBRE MESH APPLIED ONTO BASECOAT
(PRODUCT CODE: ESPS/M100 WHITE)

TOPCOAT ENVIROSIL SILICONE FINISH OVER PRIMER 1.5mm GRAIN
SILICONE PRIMER WHITE (PRODUCT CODE: ESPS/S-P/G/wh)
SILICONE TOPCOAT WHITE (PRODUCT CODE: ESPS/S-TZ/wh)
FINISH: TO BE CONFIRMED

RED LINE DENOTES TRESTARD 420 BLACK FR SEALING TAPE, 150mm WIDE

PVC MESH-WINGED CORNER ANGLE BEAD
(PRODUCT CODE: ESPS1023)

15mm WIDE EXPANDING SEALANT TAPE
(PRODUCT CODE: ESPS-SEAL15/3-7)


6mm PVC APU FRAME SEAL BEAD
(PRODUCT CODE: ESPS1060)

02 CROSS SECTION - RENDER / WINDOW HEAD INTERFACE DETAIL
Scale 1:2



FITTERS NOTE
EXISTING WINDOW SILL TO BE REMOVED & RETAINED TO ALLOW
FOR RENDER INSTALL. WINDOW SILL TO BE REINSTATED ON
COMPLETION OF RENDER WORKS.

INTERNAL NOTE
BENX SYSTEM DETAILS SHOWS 40mm WINDOW SILL
OVERHANG (MINIMUM) FROM FACE OF RENDER -
TO BE REVIEWED ON SITE

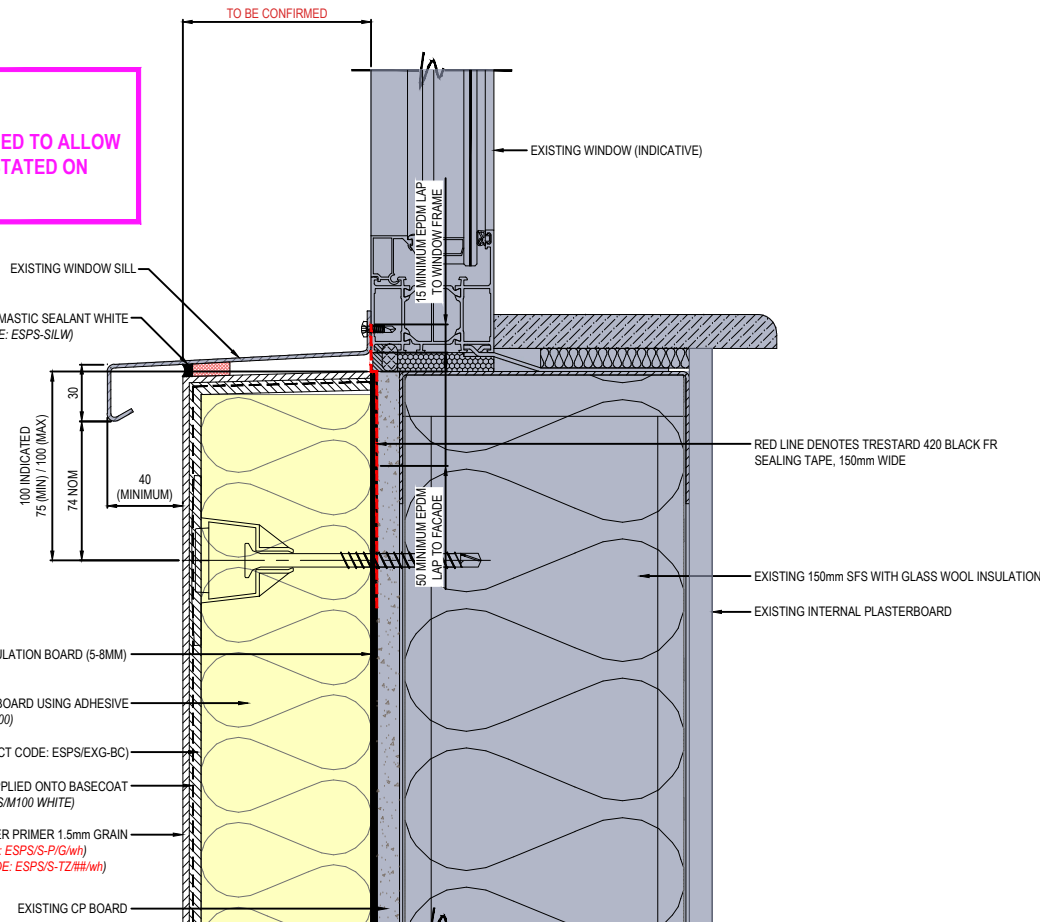

03 CROSS SECTION - RENDER / WINDOW SILL INTERFACE DETAIL
Scale 1:2



FITTERS NOTE
THIS DRAWING IS TO BE READ IN CONJUNCTION WITH RENDER
SPECIFICATION DRAWING No. TSB-RFL-ZZ-ZZ-DR-W-001201

Rev	Desc	Author	Check	Appr
01	Issue	BB	MHY	
02	Issue	BB	MHY	
03	Issue	BB	MHY	

FOR CONSTRUCTION

Client: BARRATT REDROW
Project: 1761 THE SUMMIT
Title: RENDER SYSTEM WINDOW JAMB, HEAD & SILL SECTION DETAILS
Drawn By: BB
Checked By: MHY
Scale: 1:2 @ A1
Date: 27/06/2025
TSB-RFL-ZZ-ZZ-DR-W-003001 C01